

ZAPOJENÍ NA MINISERVERU


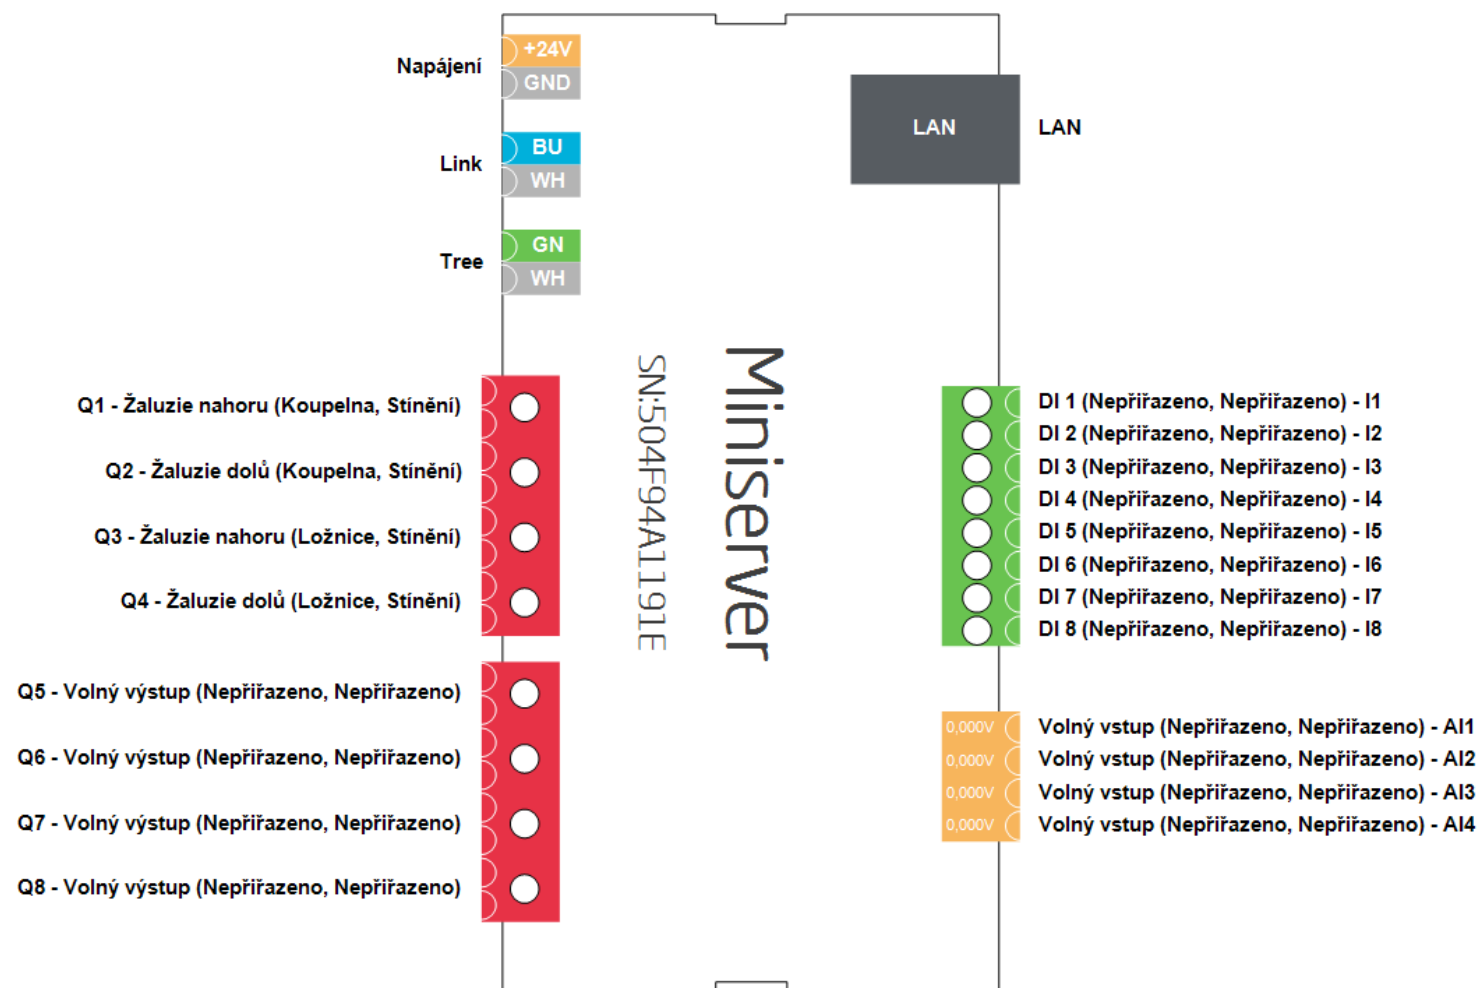


SCHÉMA PANELU



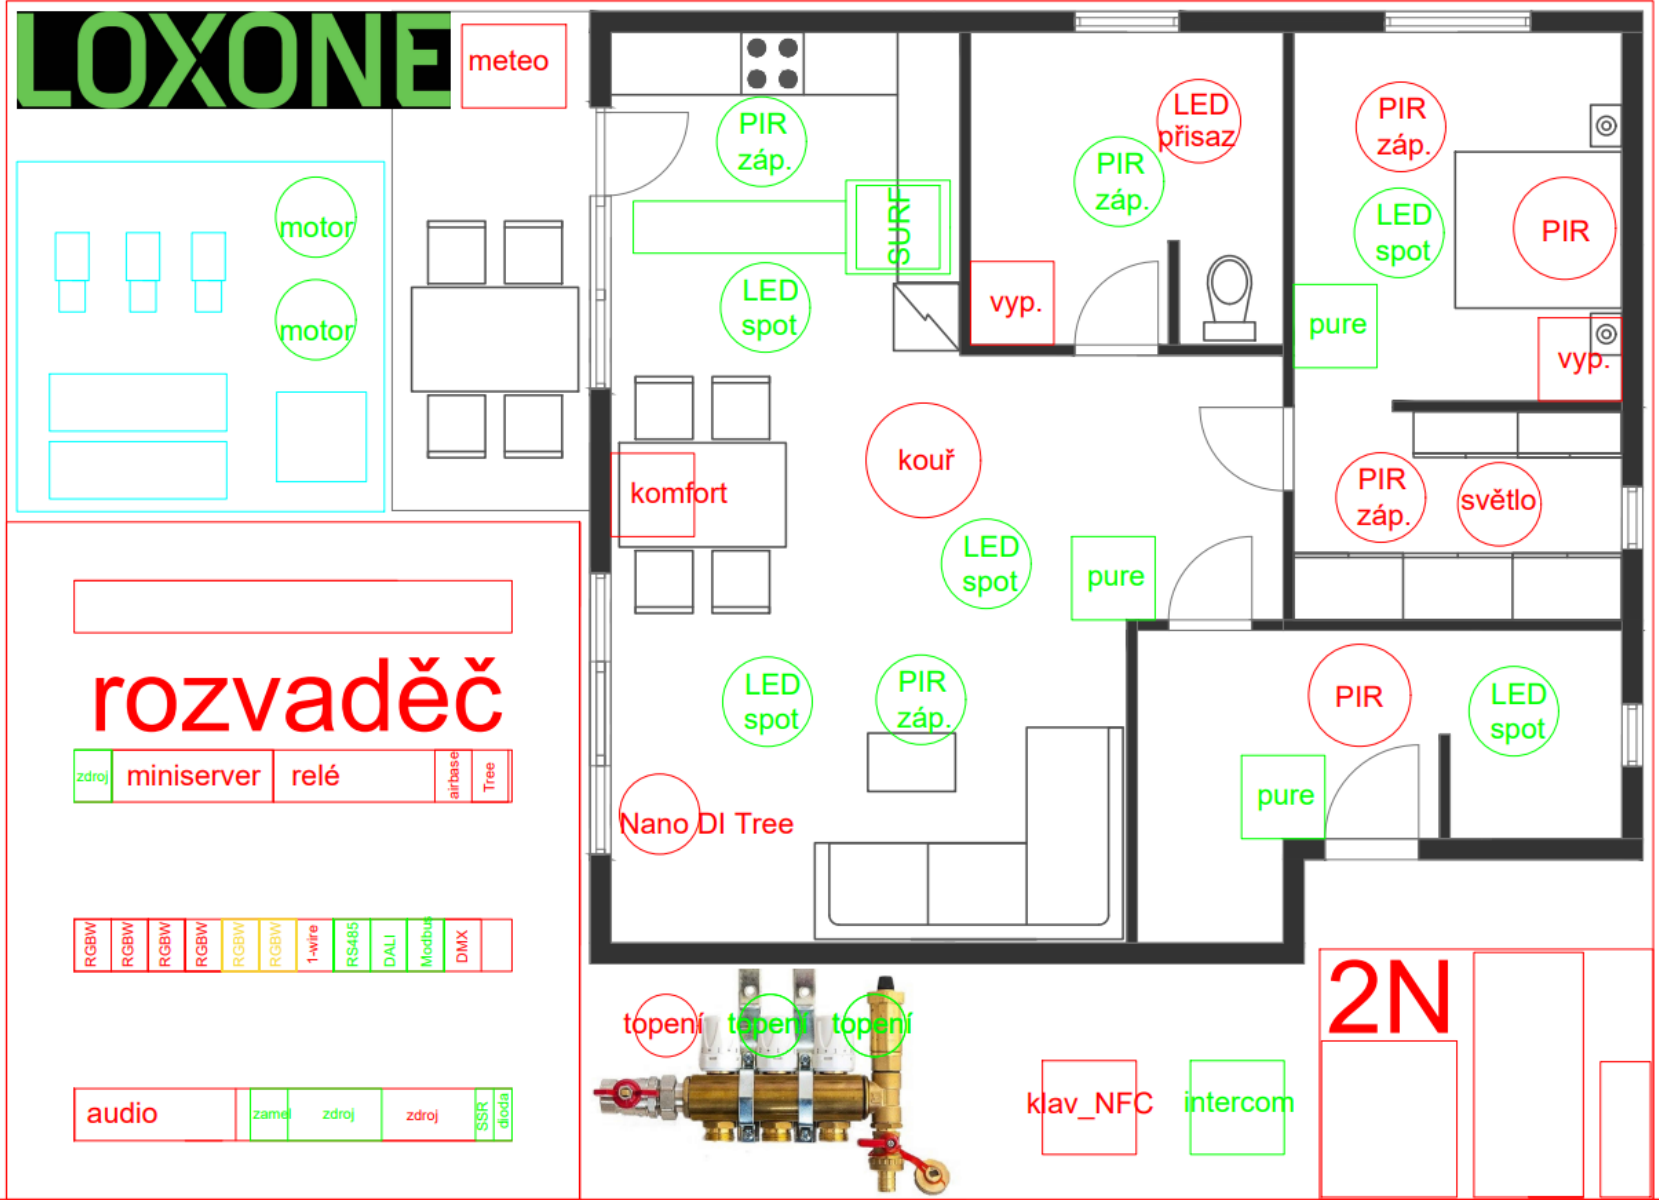

PANEL 1

MS: 10.101.1.1
AS: 10.101.1.2
INTERCOM: 10.101.1.3

PANEL 2

MS: 10.101.2.1
AS: 10.101.2.2
INTERCOM: 10.101.2.3

PANEL 3

MS: 10.101.3.1
AS: 10.101.3.2
INTERCOM: 10.101.3.3

ŽÁCI

ŽÁCI

ŽÁCI

PANEL 5

MS: 10.101.5.1
AS: 10.101.5.2
INTERCOM: 10.101.5.3

PANEL 4

MS: 10.101.4.1
AS: 10.101.4.2
INTERCOM: 10.101.4.3